

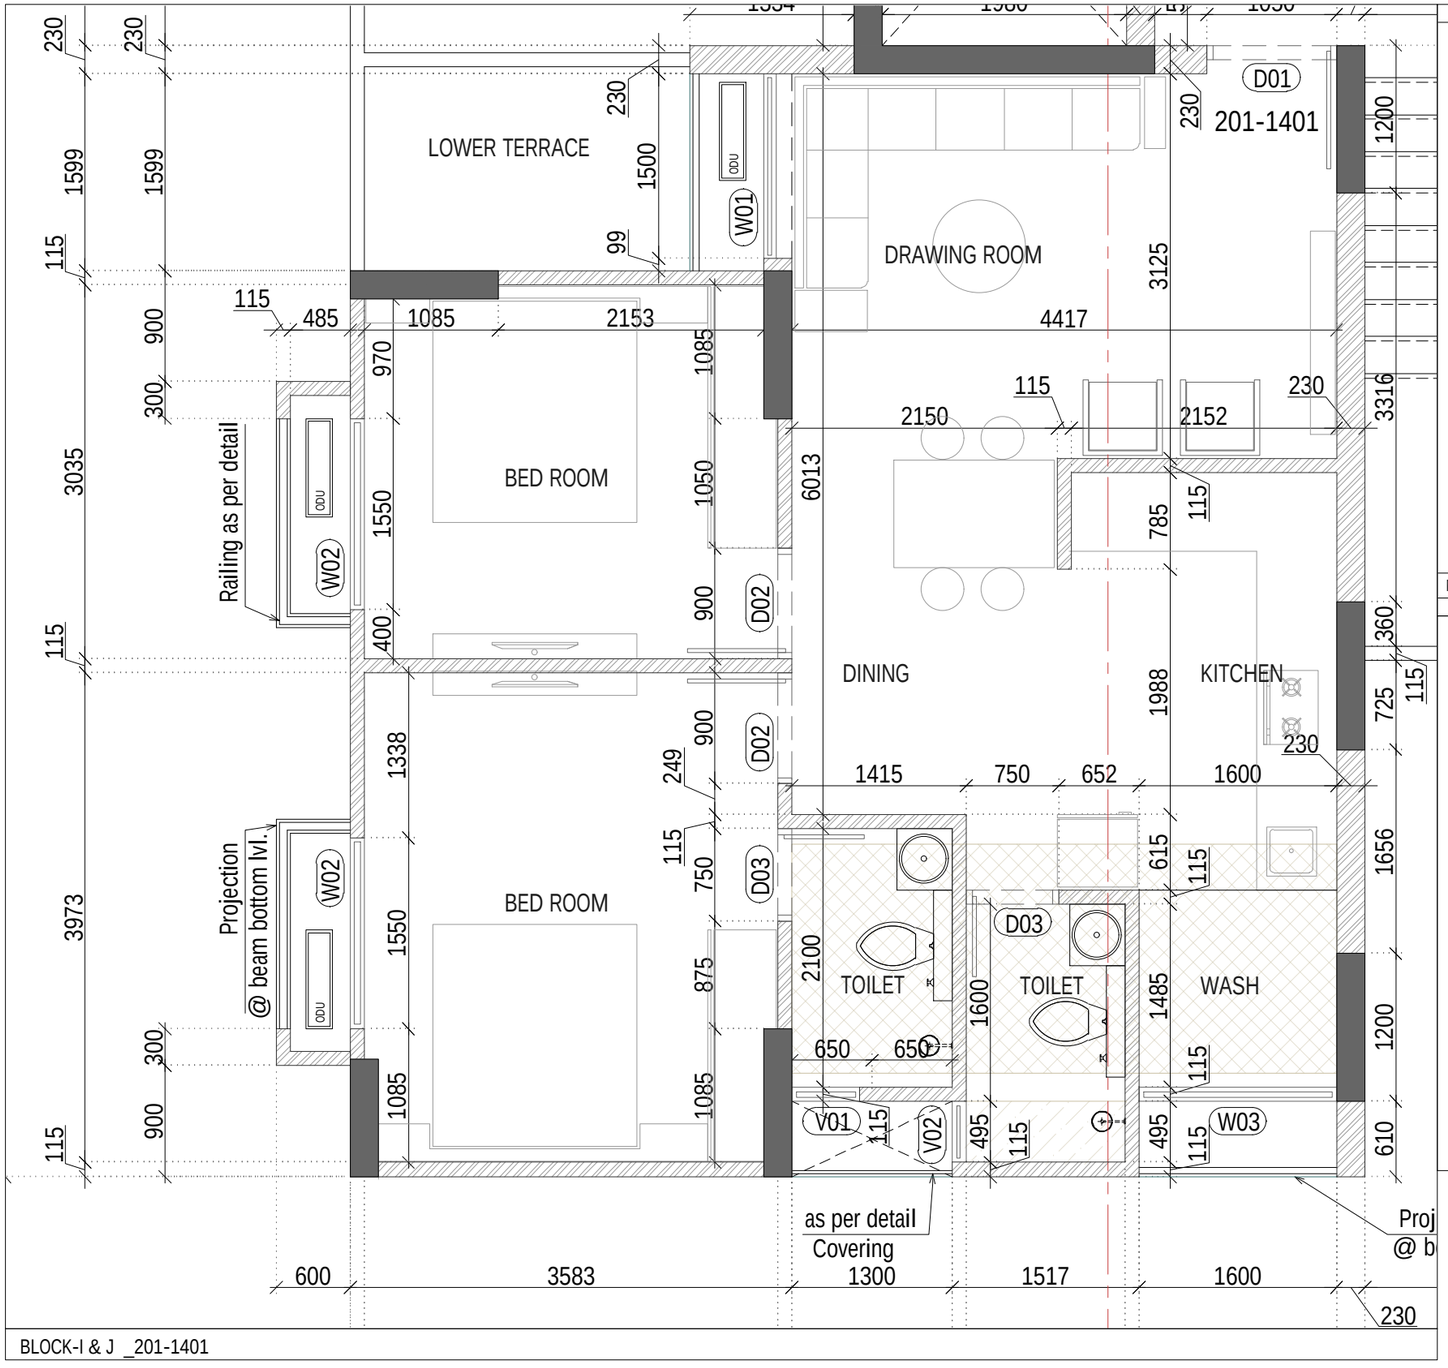


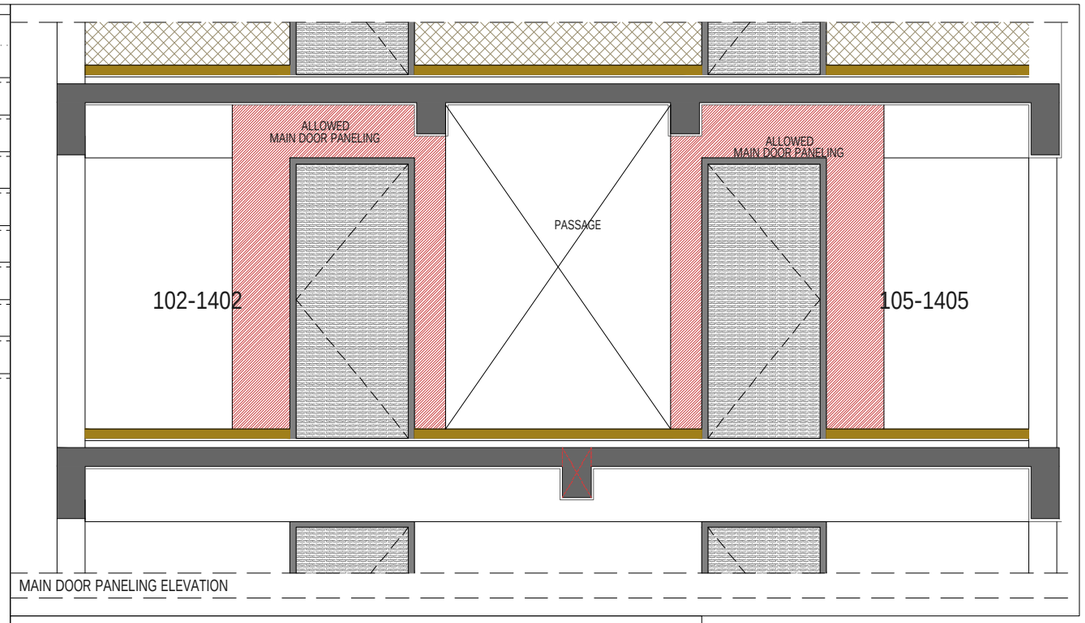

MAIN DOOR PANELING ELEVATION

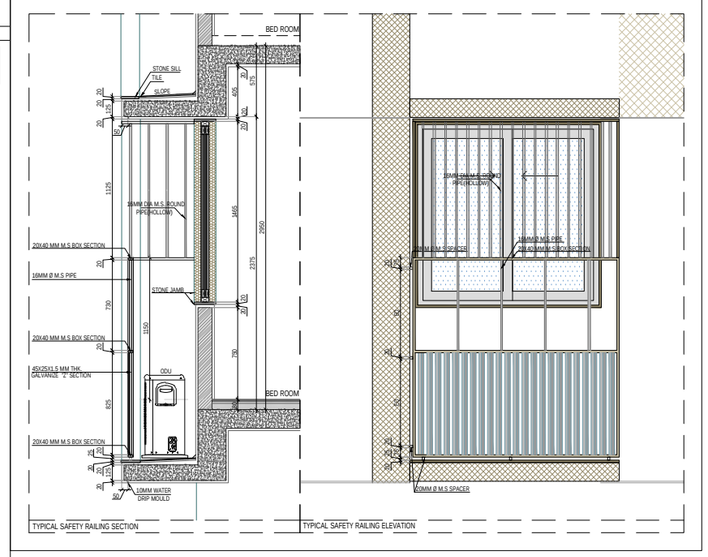

GENERAL NOTES

1) ALL DIMENSIONS ARE IN MILLIMETER.
2) ALL MEASUREMENTS ARE FROM UNFINISHED SURFACE TO UNFINISHED SURFACE.
3) ALL DIMENSIONS ARE TO BE READ AND NOT TO BE MEASURED.
4) IN CASE OF ANY DISCREPANCY BETWEEN ARCHITECTURAL DRGS AND OTHER DRGS., DISCREPANCY SHOULD BE BROUGHT TO THE NOTICE OF THE ARCHITECT BEFORE COMMENCEMENT OF THE WORK.
5) IN CASE OF ANY AMBIGUITIES ON SITE,THE ARCHITECT SHOULD BE INFORMED.
6) IT IS MUST TO INFORM AND TO HAVE PRIOR PERMISSION OF ARCHITECT BEFORE MAKING ANY CHANGES ON SITE.
7) REFER THE LATEST REVISED DRAWING.
8) BEFORE COMMENCING THE WORK IT IS MUST TO OBTAIN PRIOR PERMISSION FROM THE CONCERNED MUNICIPAL CORPORATION.
9) SOIL TESTING TO BE CARRIED OUT BEFORE COMMENCEMENT OF THE FOUNDATION.
10) IT IS MUST FOR RESPECTIVE SITE ENGINEER TO CHECK AND CO-RELATE THE CONTOUR LVL. OF THE SURVEY DRAWINGS WITH THE CONTOUR LVL. OF THE ARCHITECTURAL DRAWINGS.
11) IT IS MUST FOR RESPECTIVE SITE ENGINEER TO KEEP IN MIND THAT THE OUTER REFERENCE NODES OF THE BOUNDARY WHICH ARE TAKEN IN TO CONSIDERATION IN THE ARCHITECTURAL DRG. - FOR THE BUILDING LOCATION ON THE SITE, ARE AS PER THE NODES GIVEN BY THE SURVEY DRAWING.
12) FOUNDATION & U.G.W.T DETAILS TO BE APPROVED FROM STRUCTURAL ENGINEER.
13) IT IS MUST FOR RESPECTIVE SITE ENGINEER TO CHECK AND CO-RELATE THE STRUCTURAL DRAWINGS WITH ARCHITECTURAL DRAWINGS.
14) IT IS MUST FOR RESPECTIVE SITE ENGINEER TO CHECK AND CO-RELATE THE MEPF DRAWINGS WITH ARCHITECTURAL DRAWINGS.

Legend:

Key Plan:

Note:
.

Project:
SUN FOOTPRINTS

Client:
SUN BUILDER

Project No:
A-1012

Revision Notes:

Rev	Purpose of Issue	Date	Authorized
R0	Only for Review	24-02-2026	MSA

Architect :
e:studio@mansishah.co.in
1215, Avenue One,
Near Shreyas Foundation
Ambawadi, Ahmedabad-380006
mansi shah ARCHITECTS

Drawing Title :
FIRST FLOOR UNIT PLAN_BLOCK-I & J_201-1401

Drawn:	Checked:	Size:	Dwg Number:
RAMESH	MAYUR	A3	****
Date : 24-02-2026	Date : 24-02-2026	Scale: 1:50	Revision: R0

Purpose:
FOR REVIEW

Stamp:

Disclaimer: This drawing and the design/data therein are the property of Mansi Shah Architects. They are merely loaned and will neither be reproduced, copied, loaned, exhibited not used except in the limited way and private use as permitted by any written consent given by Mansi Shah Architects to the borrower.